




ARCHITECTURAL DRAWINGS

TECHNICAL DRAWINGS

STRUTTURA CONCETTI

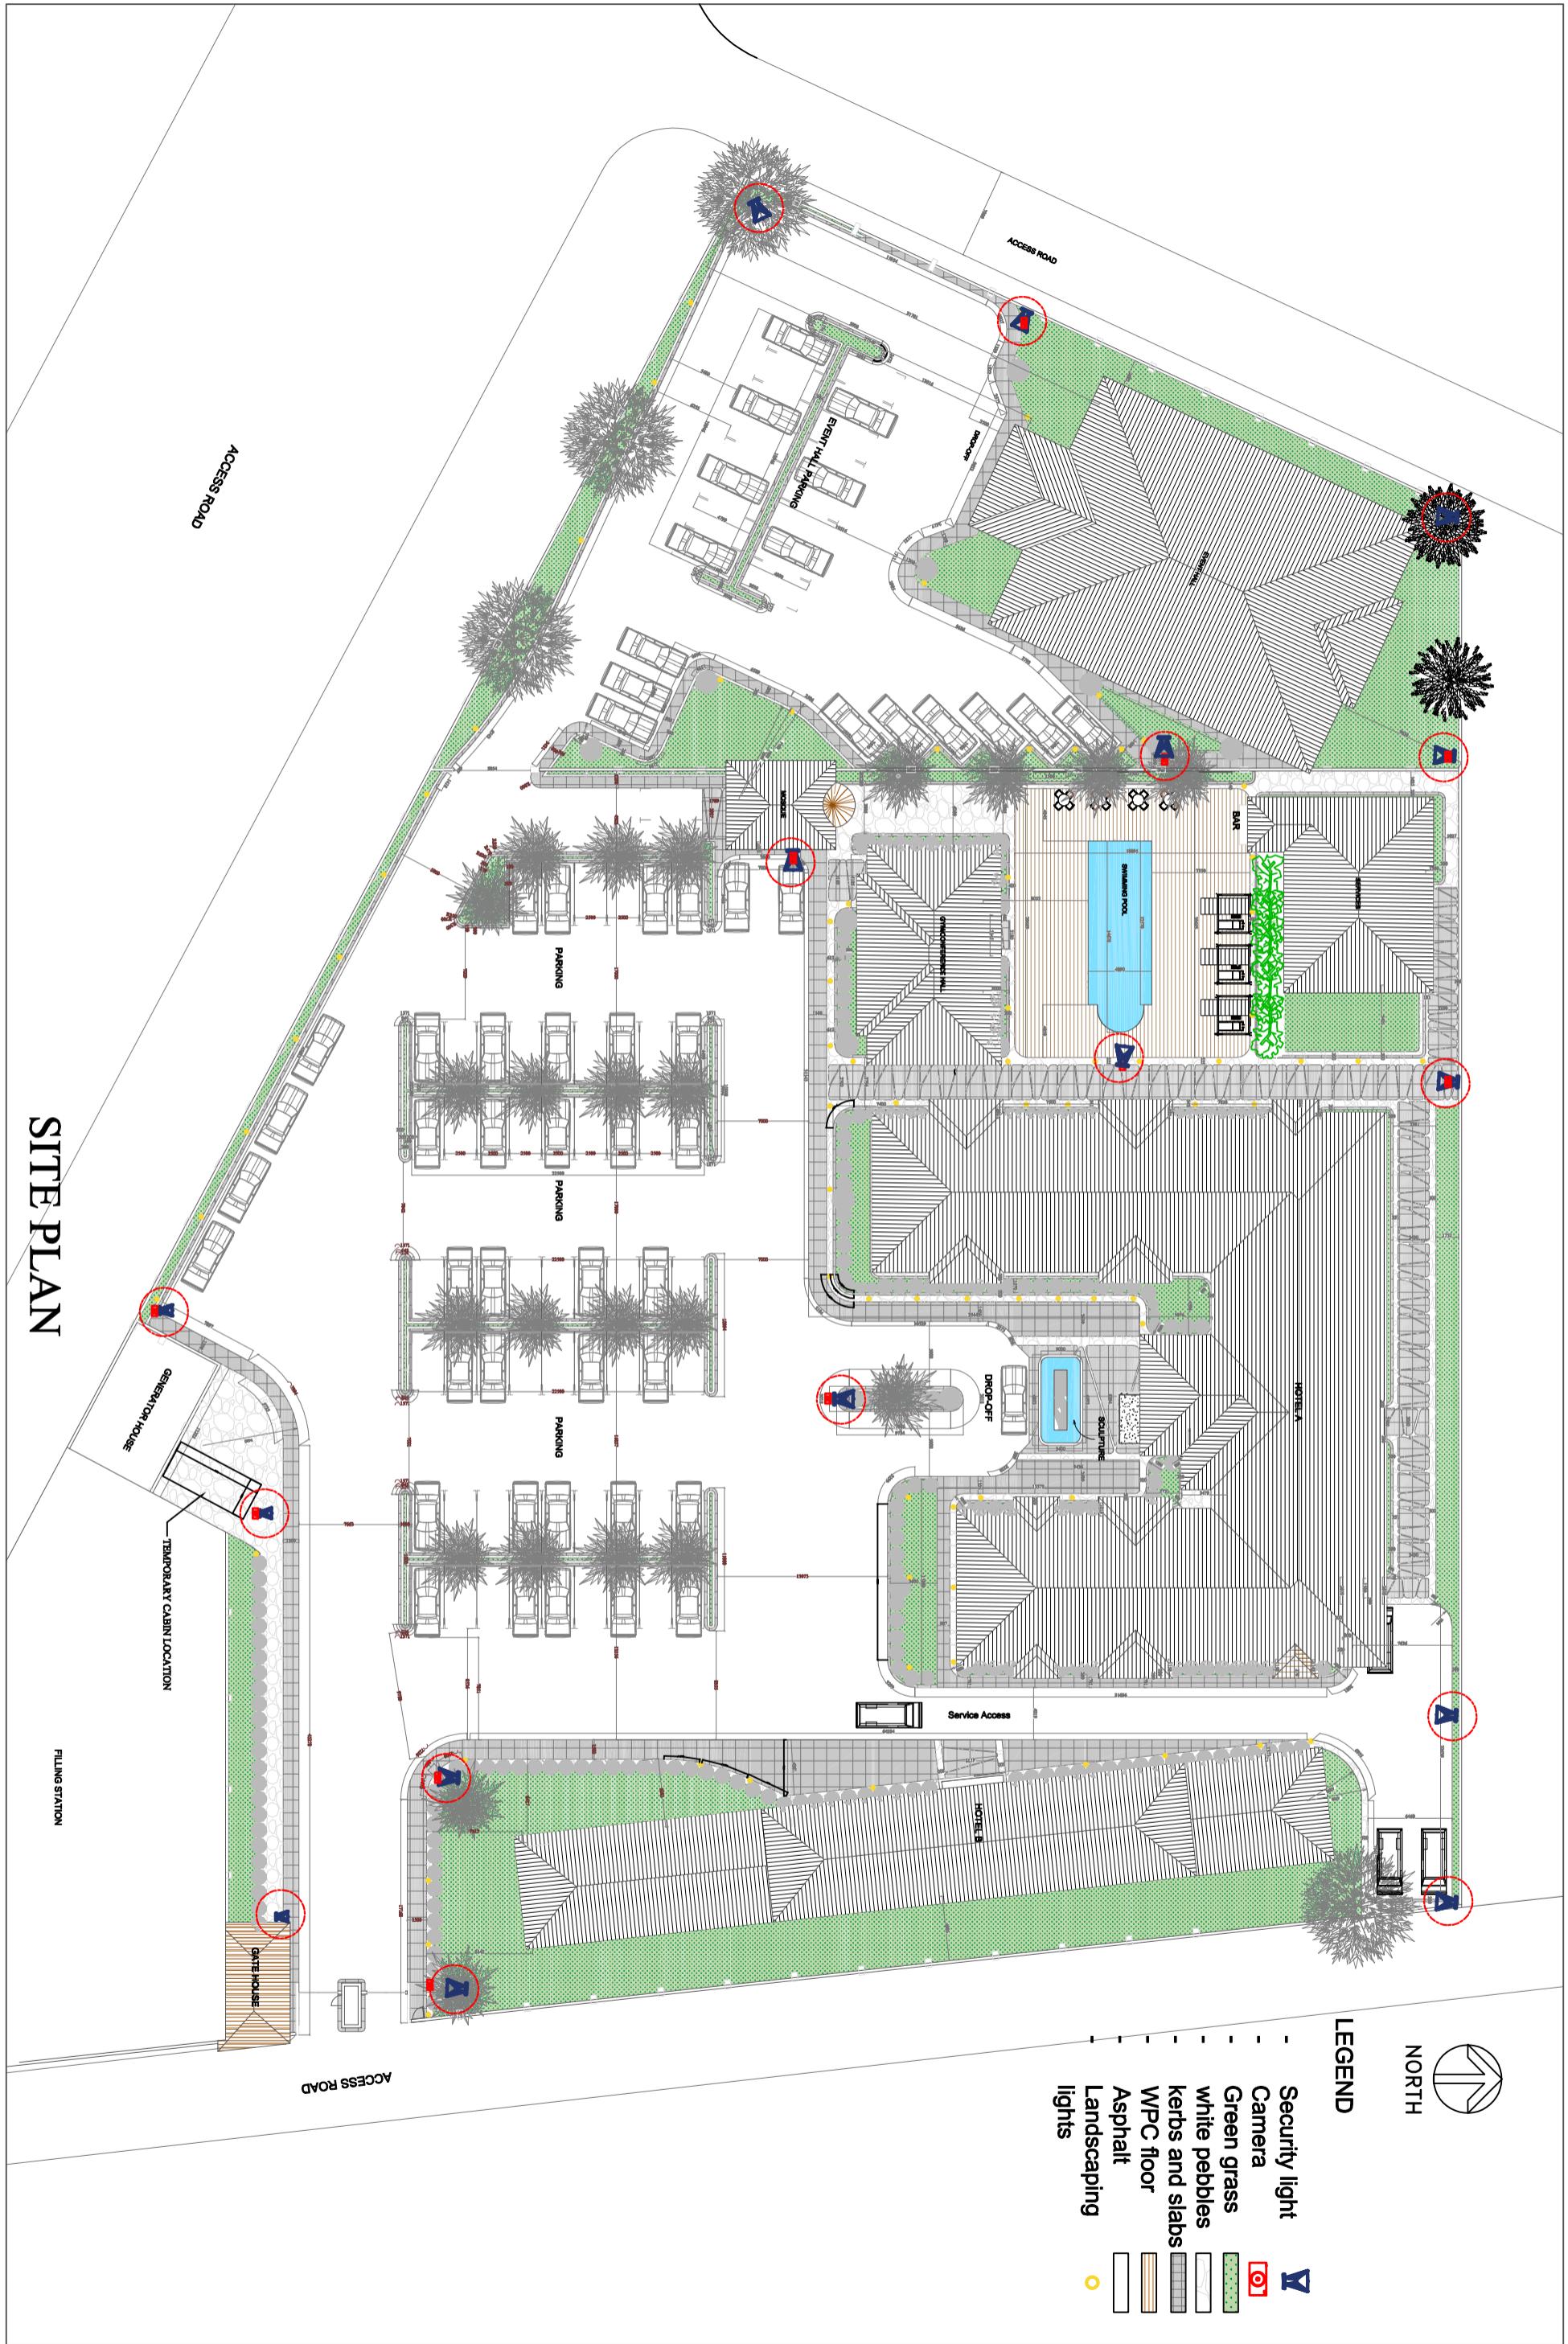

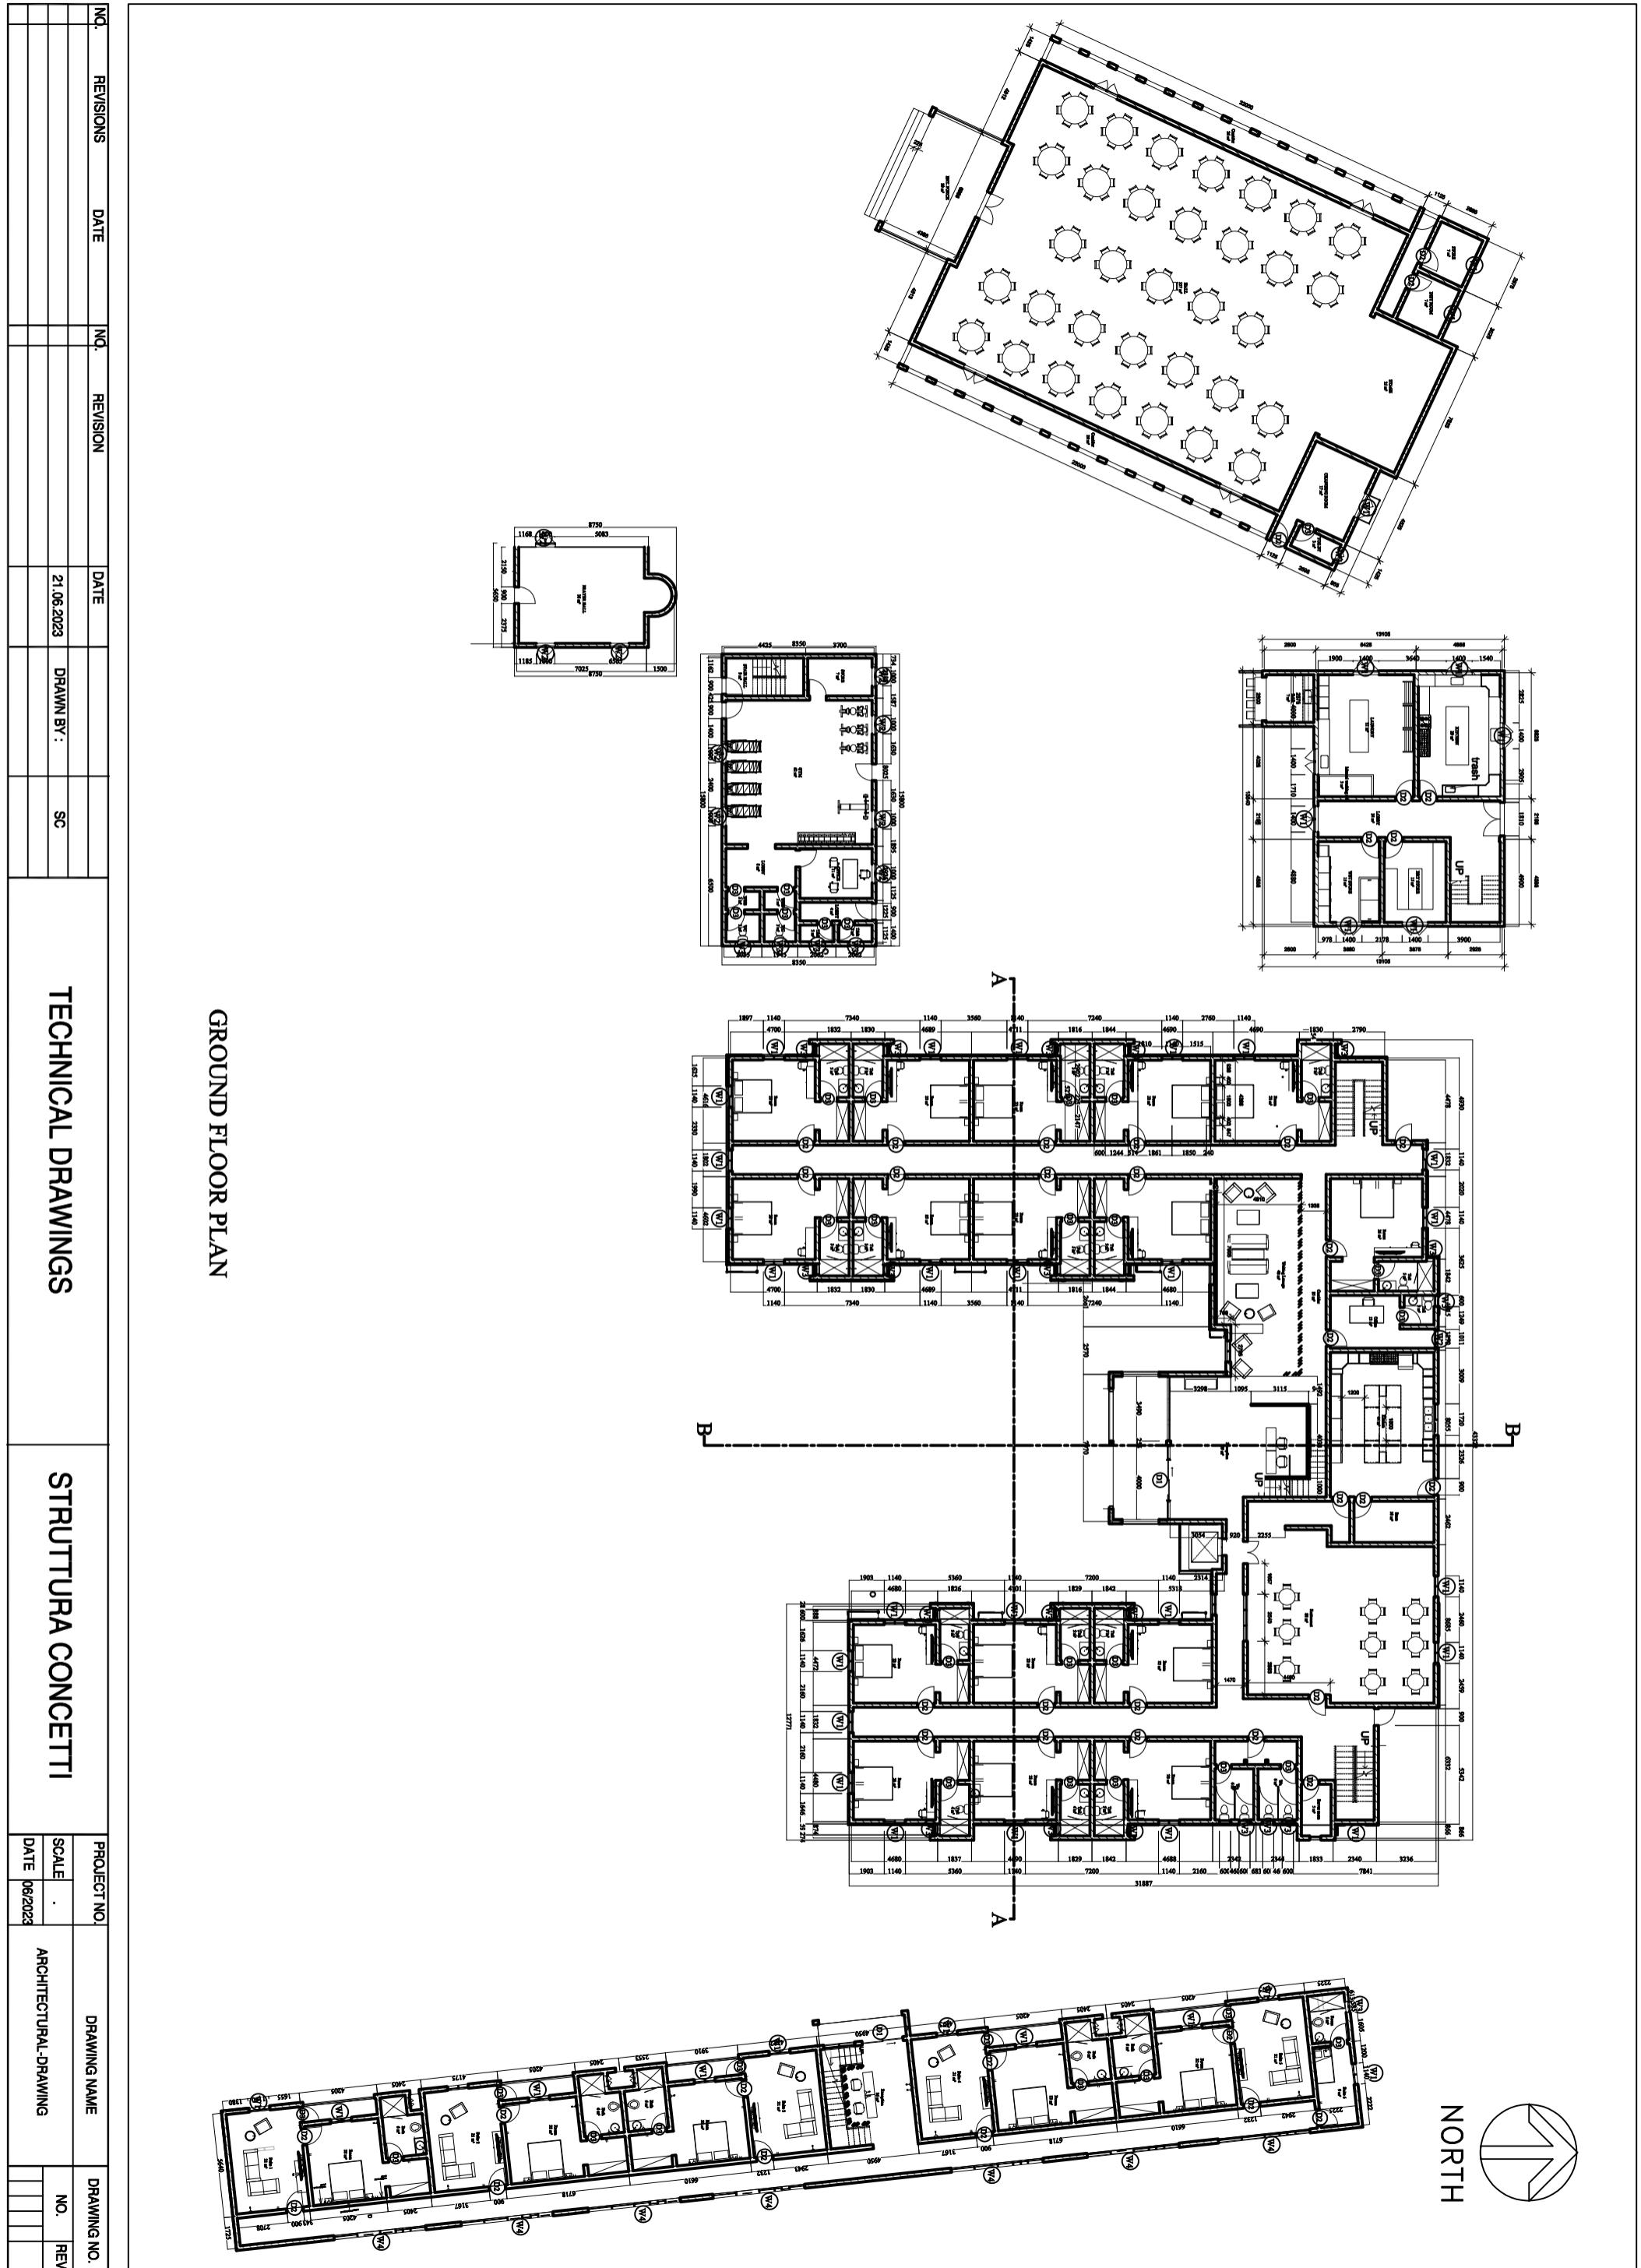





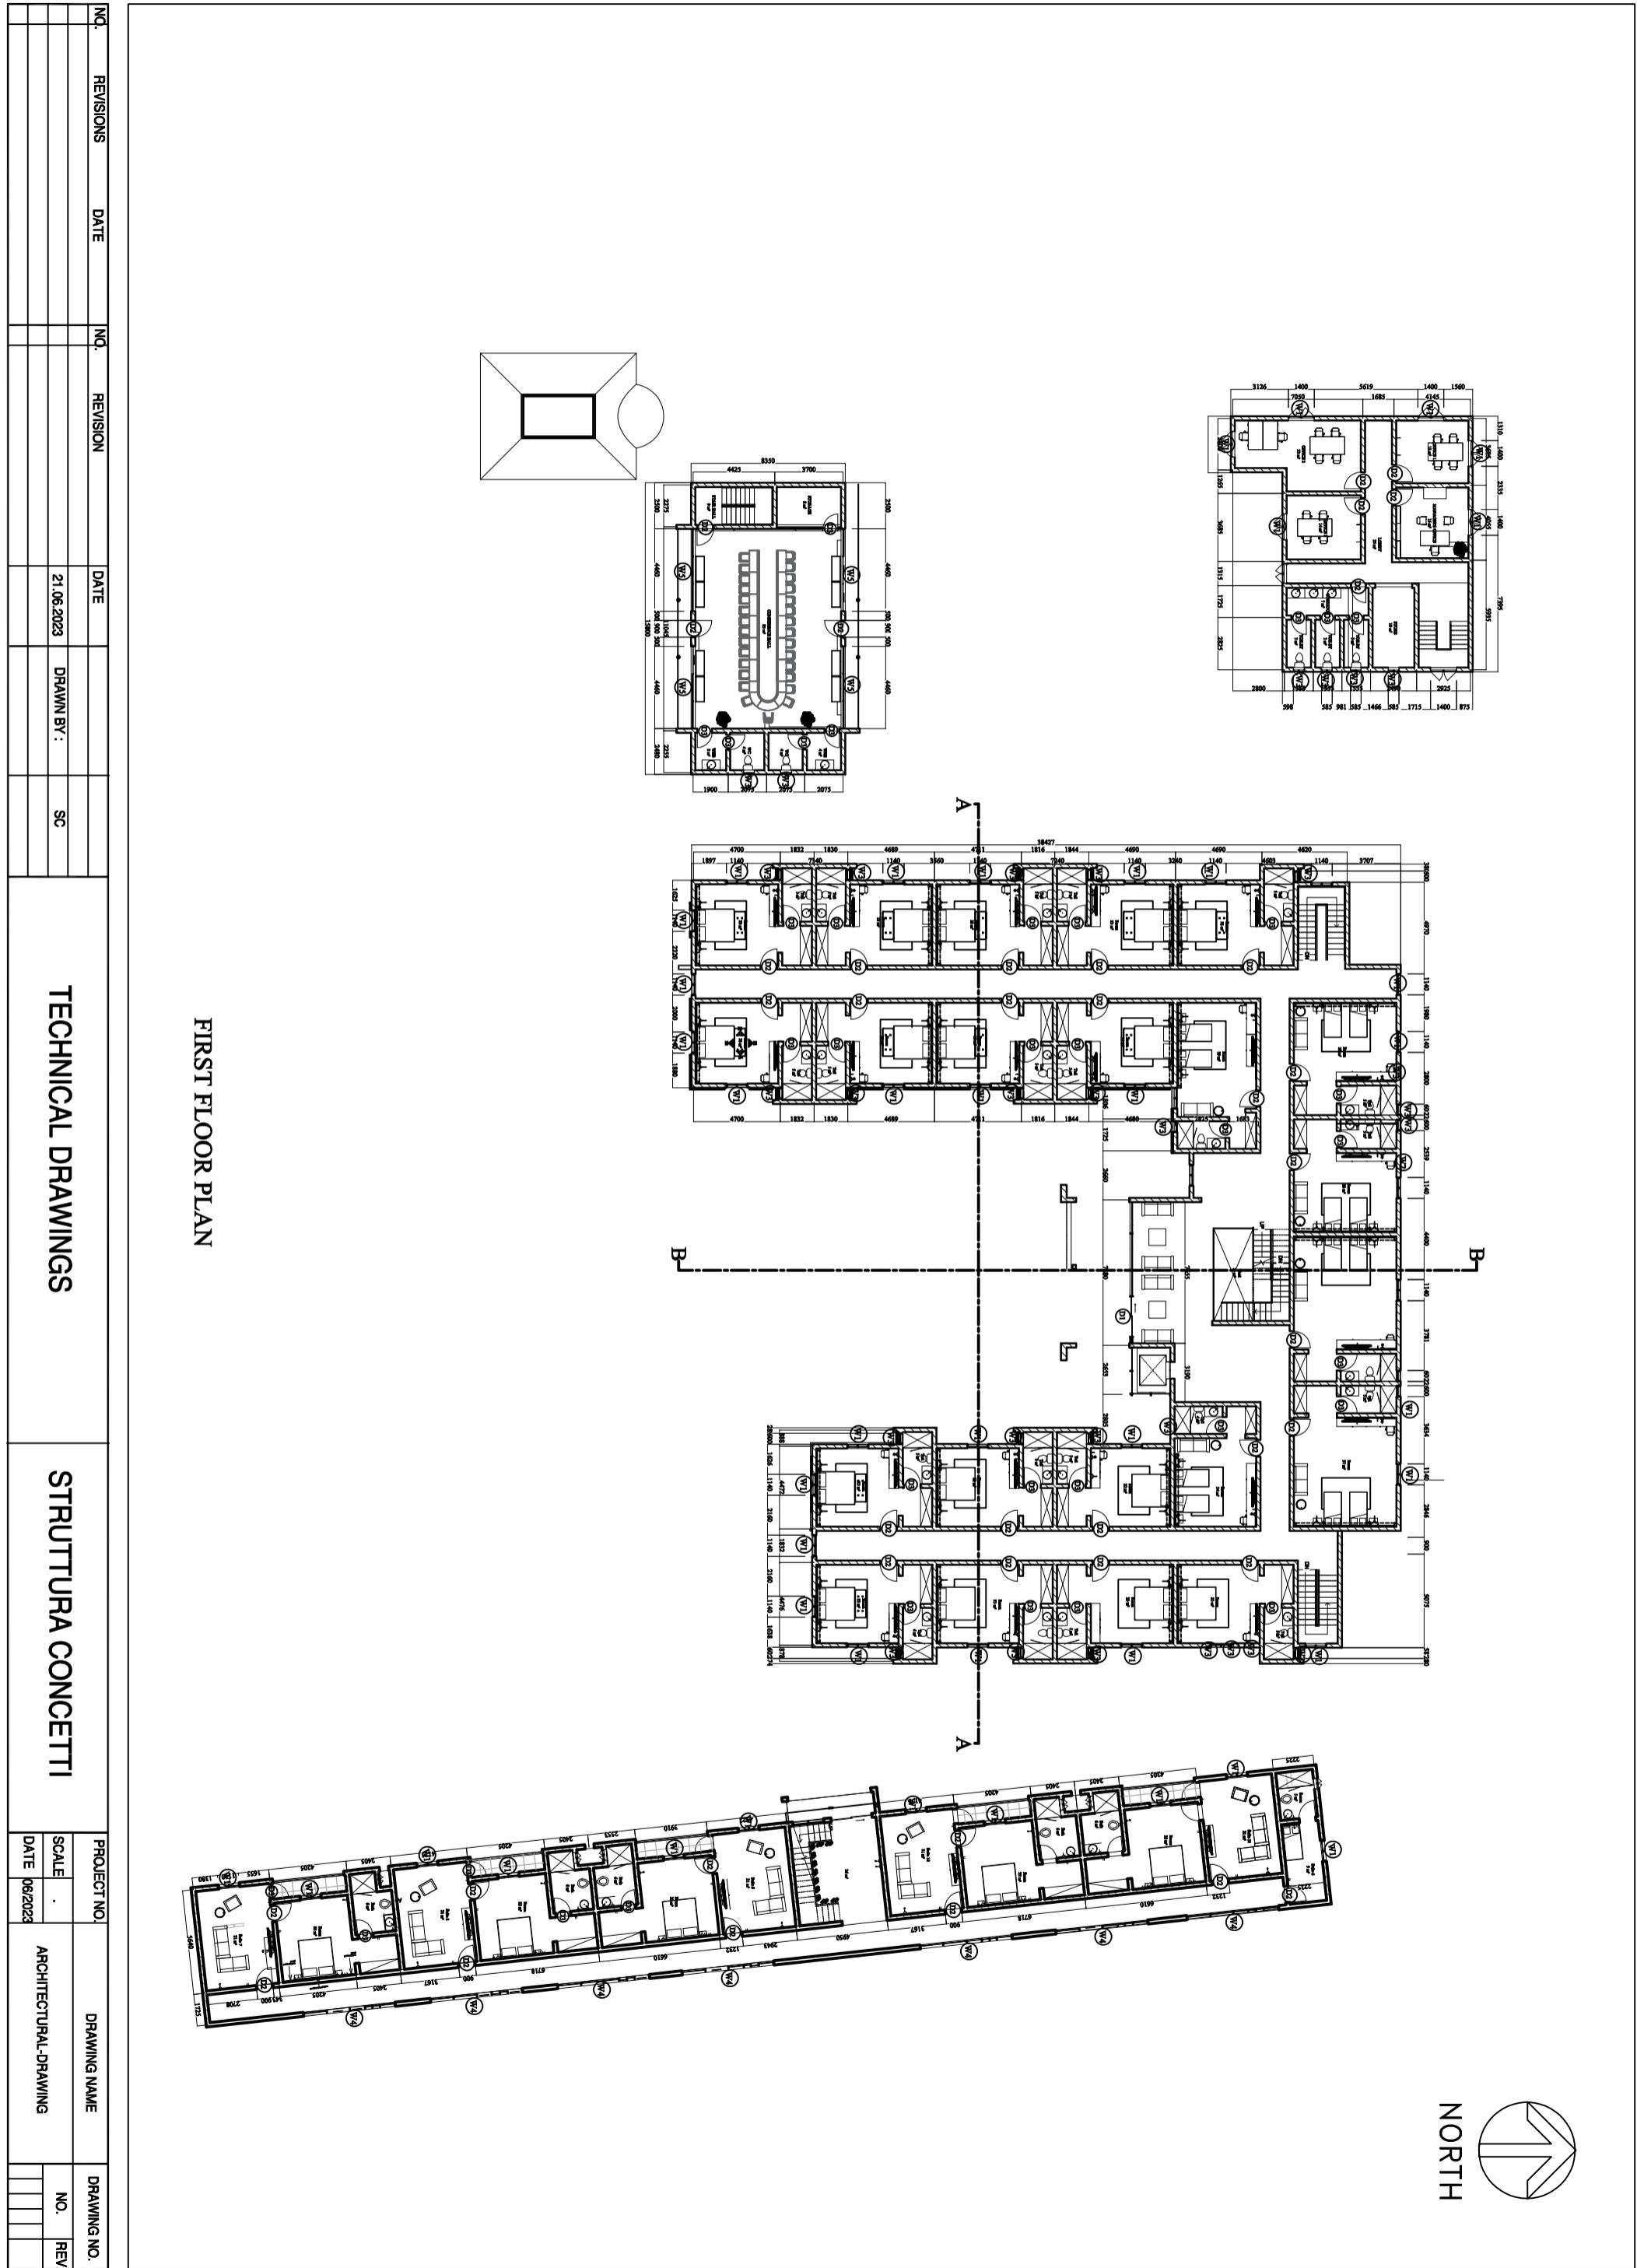


TECHNICAL DRAWINGS

STRUTTURA CONCETTI


STRUTTURA CONCETTI		PROJECT NO.	DRAWING NAME	DRAWING NO.	
SCALE	DATE	.	ARCHITECTURAL-DRAWING	NO.	REV.
	06/2023				

SECOND FLOOR PLAN

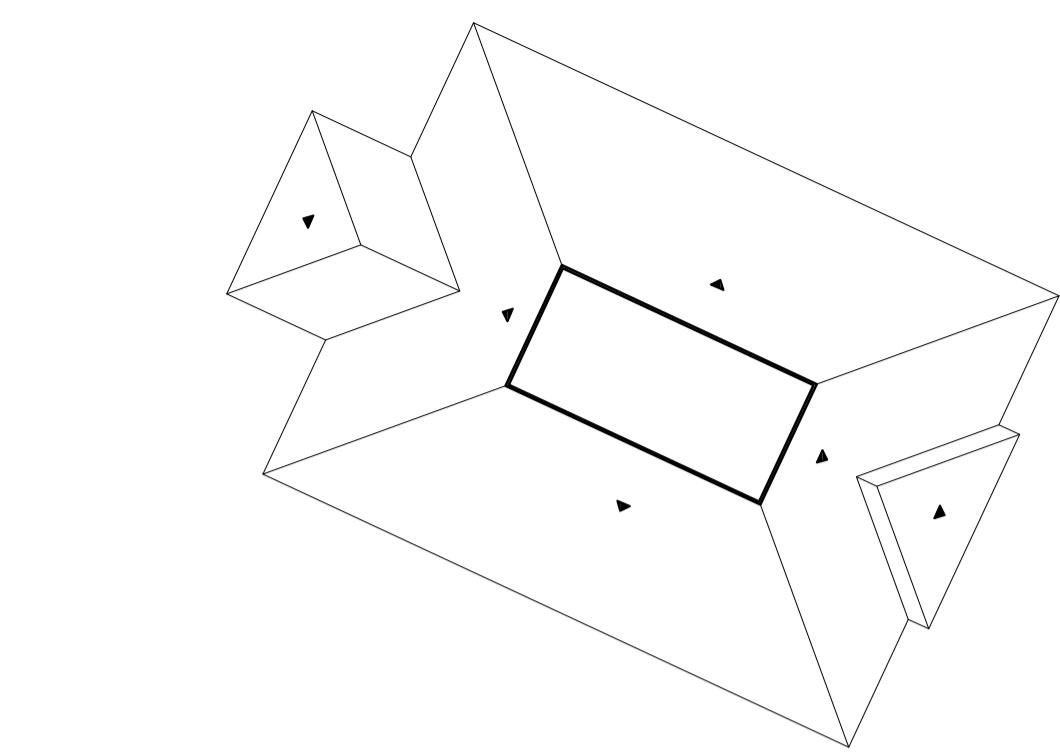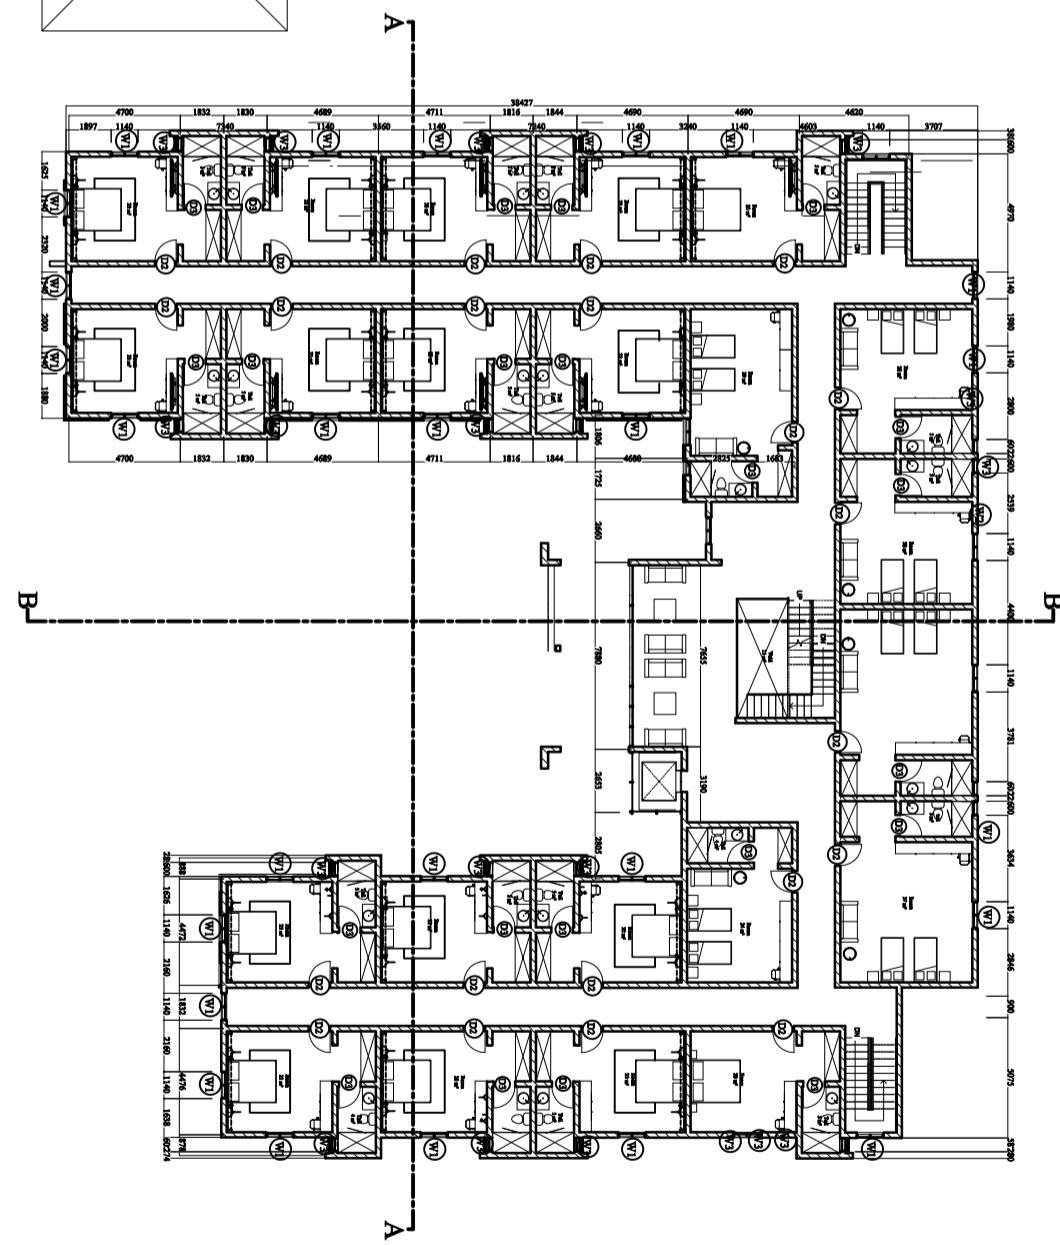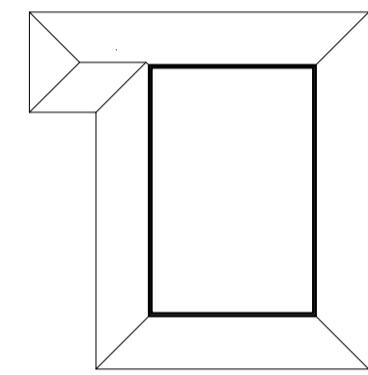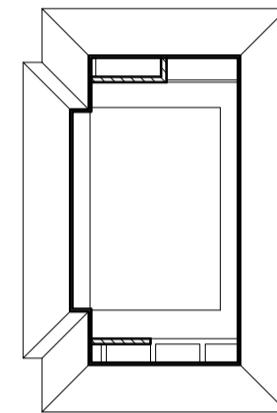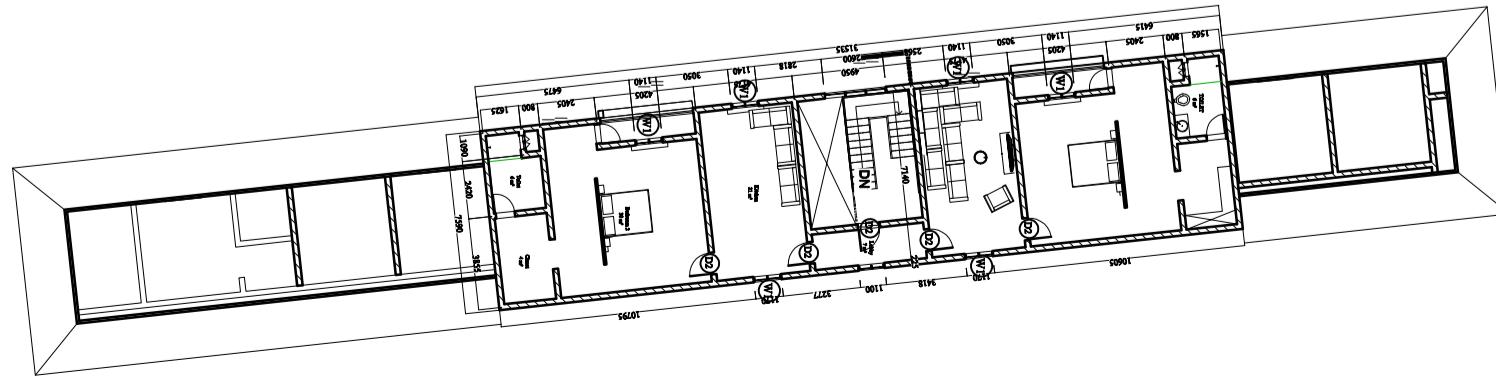


NORTH

GROUND FLOOR CEILING AND LIGHT PLAN


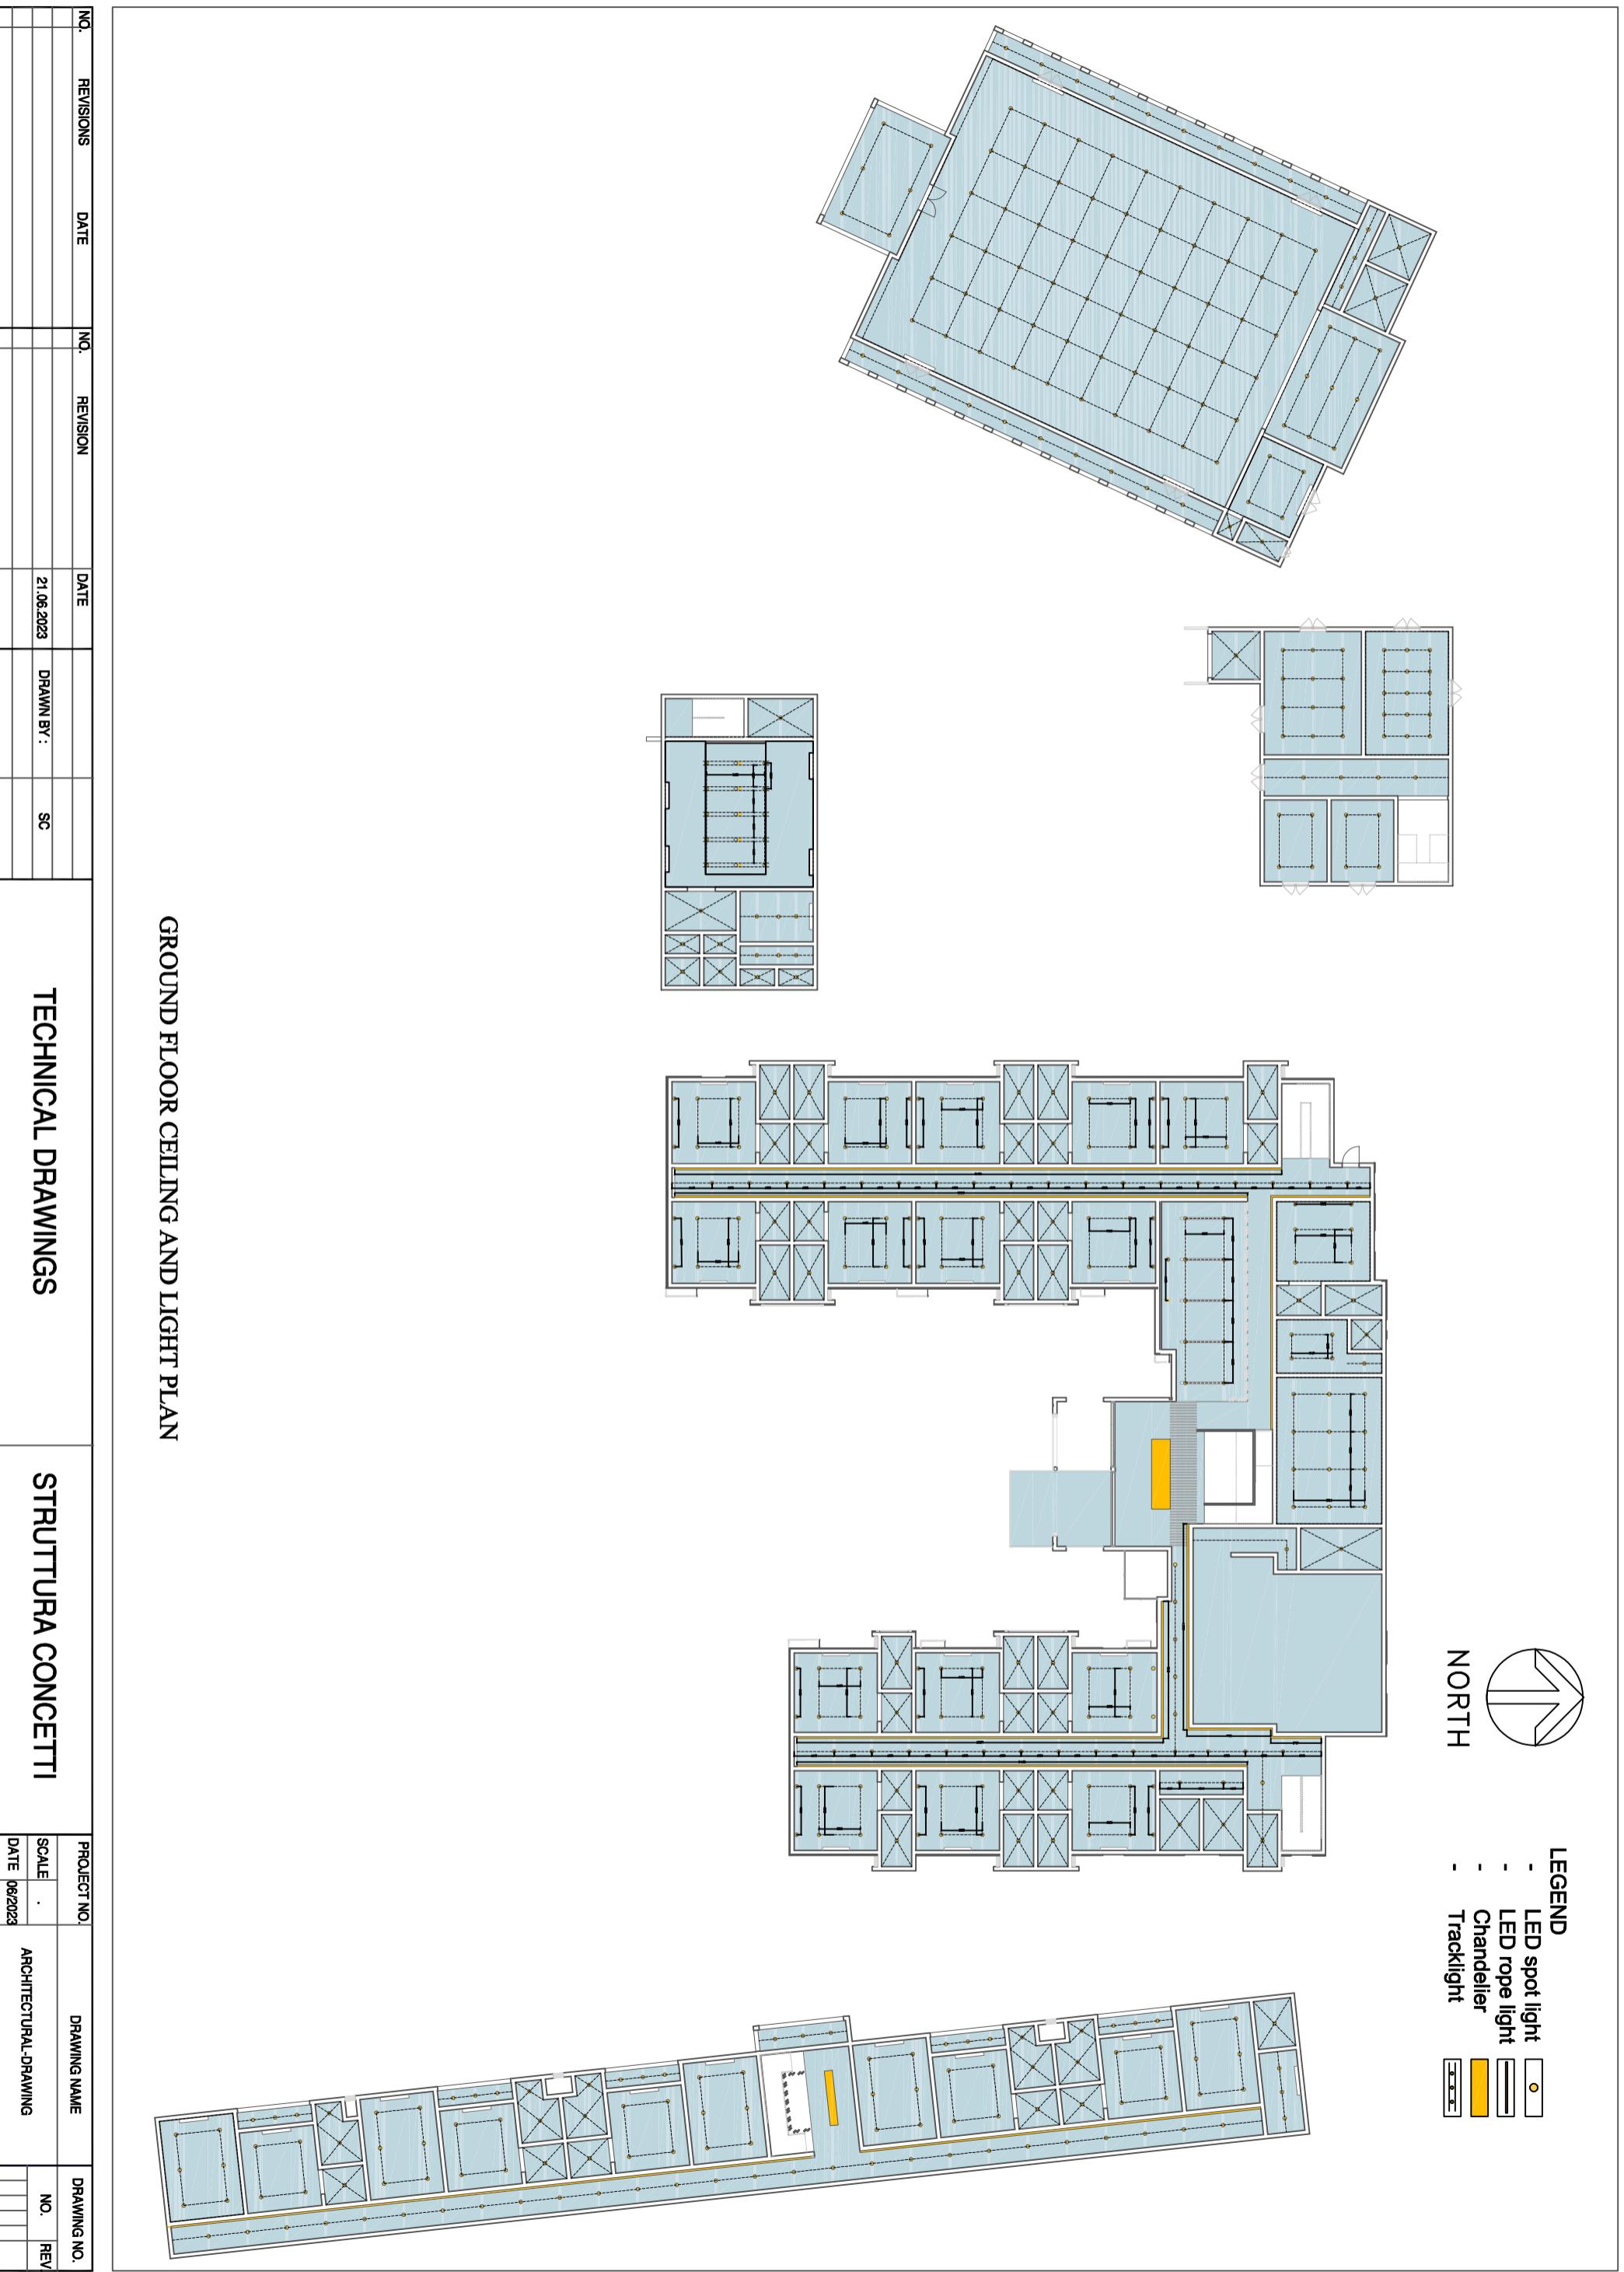


FIRST FLOOR CEILING AND LIGHT PLAN

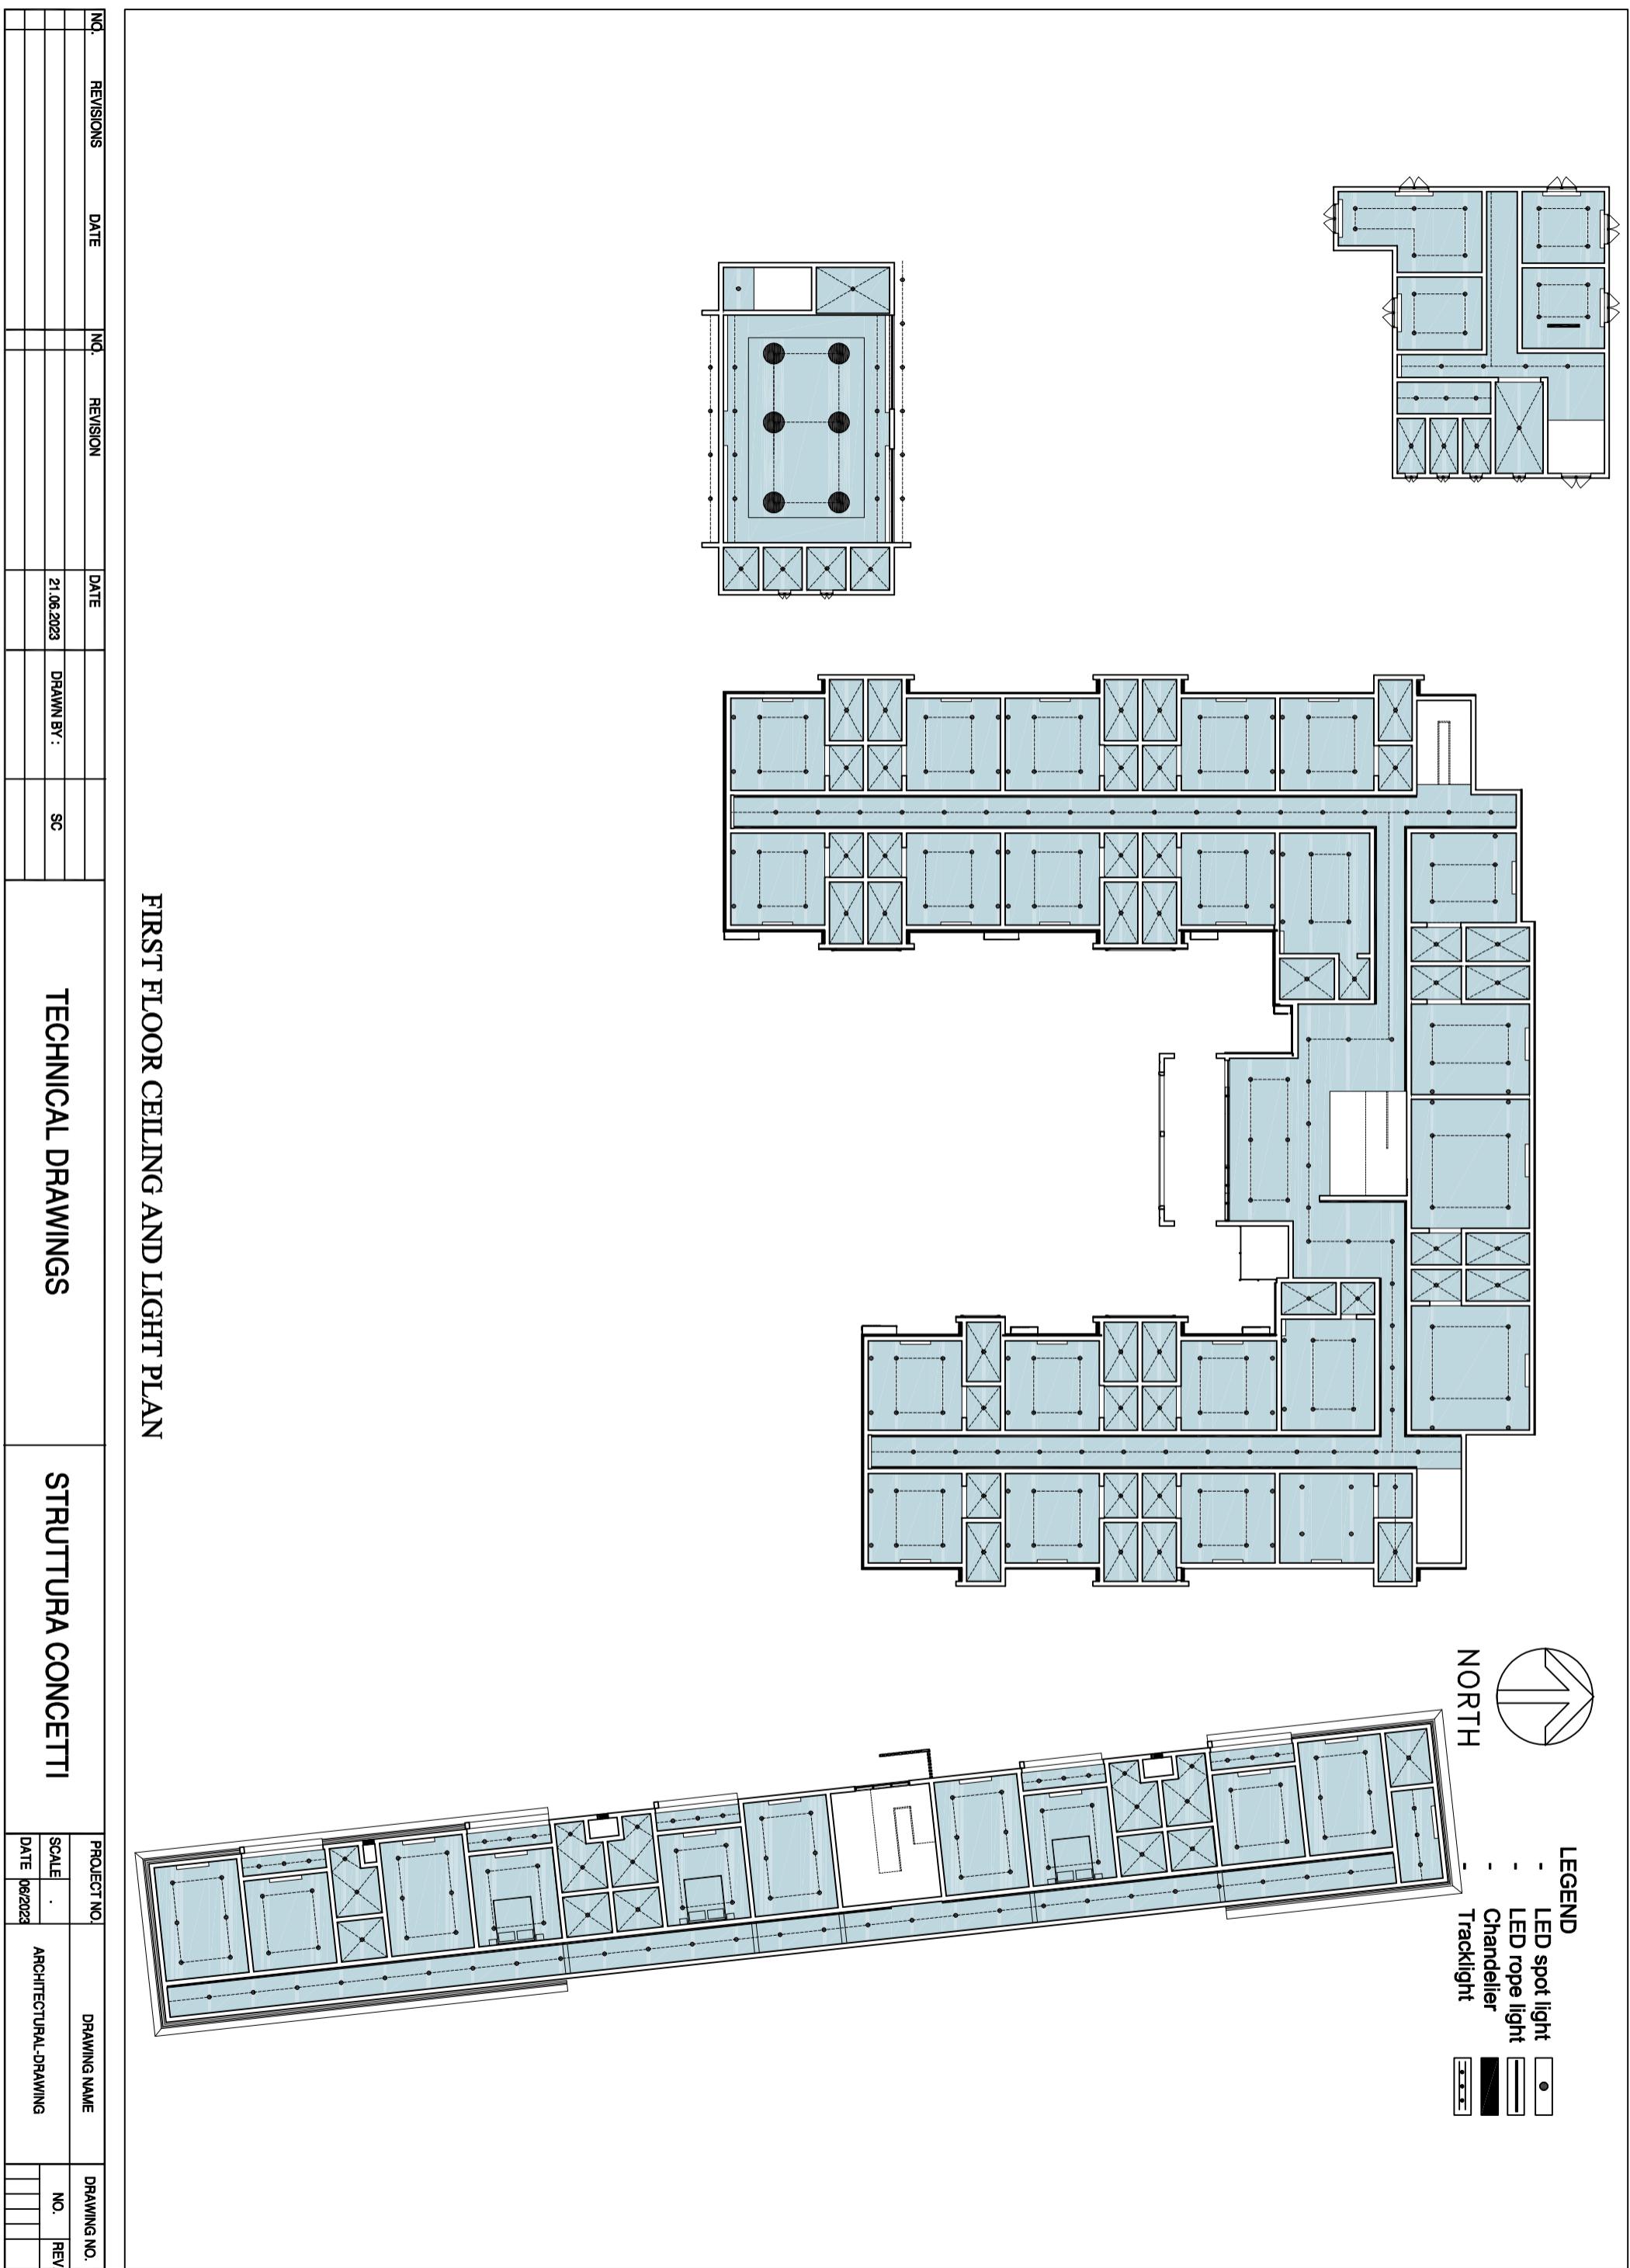

SECOND FLOOR CEILING AND LIGHT PLAN


NO.	REVISIONS	DATE	NO.	REVISION	DATE			
			DRAWN BY :					
			SC					
TECHNICAL DRAWINGS								
STRUTTURA CONCETTI								
PROJECT NO.		DRAWING NAME		DRAWING NO.				
SCALE	.	ARCHITECTURAL-DRAWING		NO.	REV.			
DATE	06/2023							

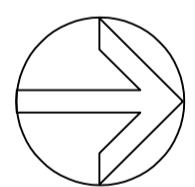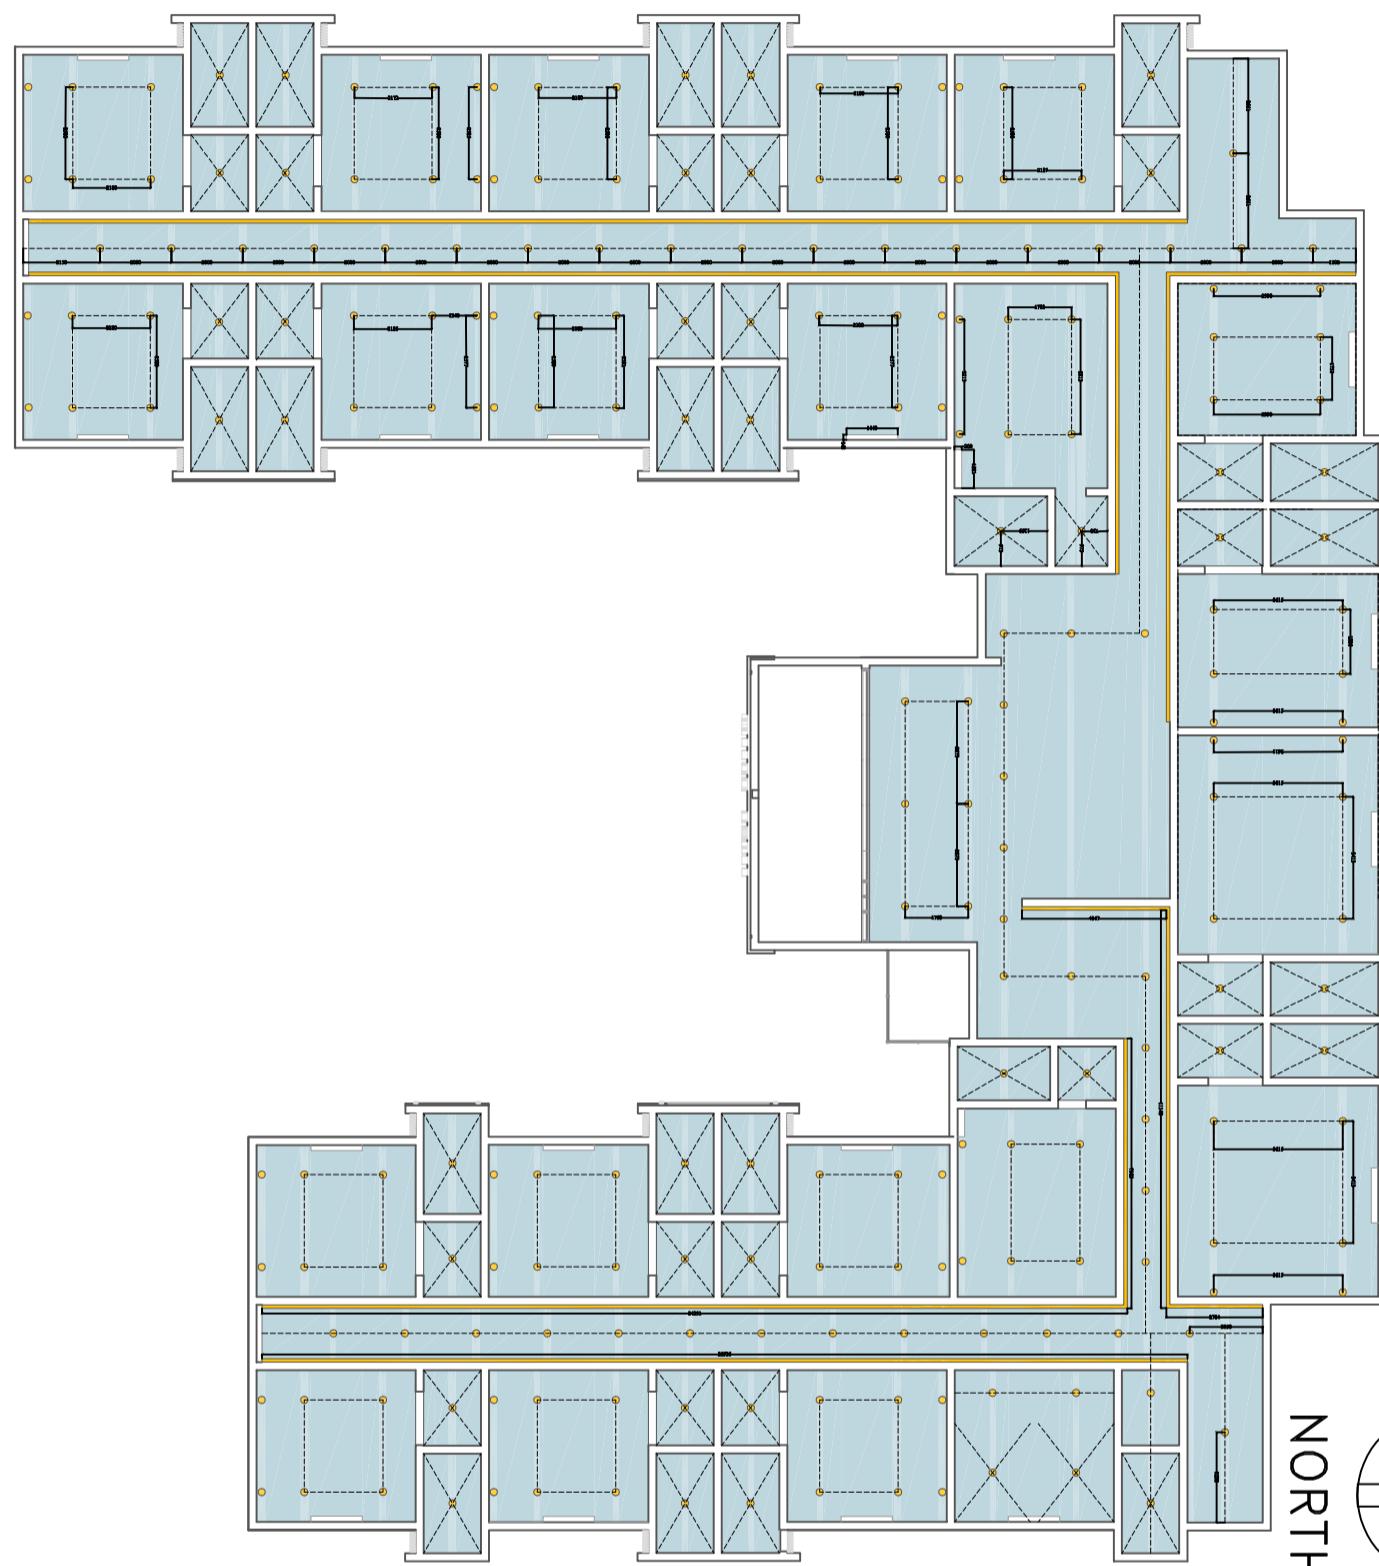

NORTH

TECHNICAL DRAWINGS

STRUTTURA CONCETTI

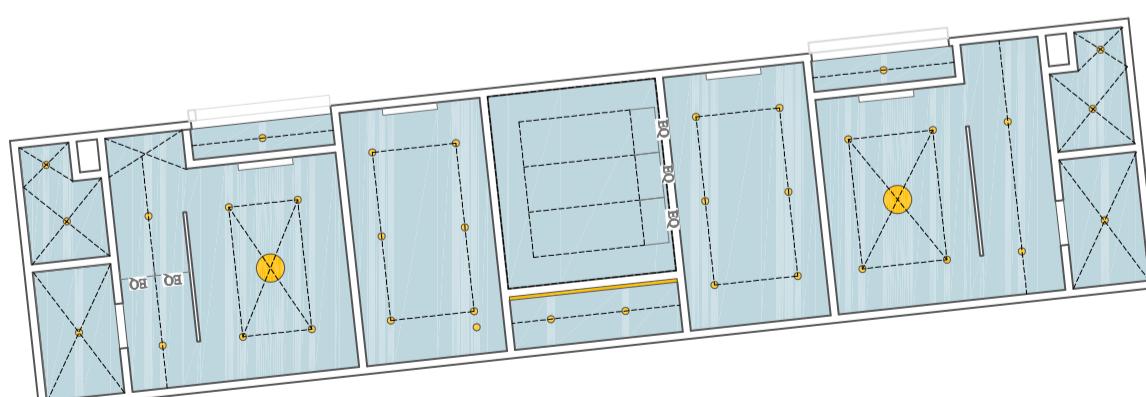

LEGEND


- LED spot light
LED rope light
Chandelier
Tracklight

NO. REVISIONS	DATE	NO. REVISION	DATE		
				DRAWN BY:	SC
PROJECT NO.	2001	DRAWING NAME	DRAWING NO.		
SCALE	.	DOOR-AND-WINDOW-SCHEDULE	NO.	REV.	
DATE	5/2023				


PROPOSED DEVELOPMENT

STRUTTURA CONCETTI

SECTION A-A

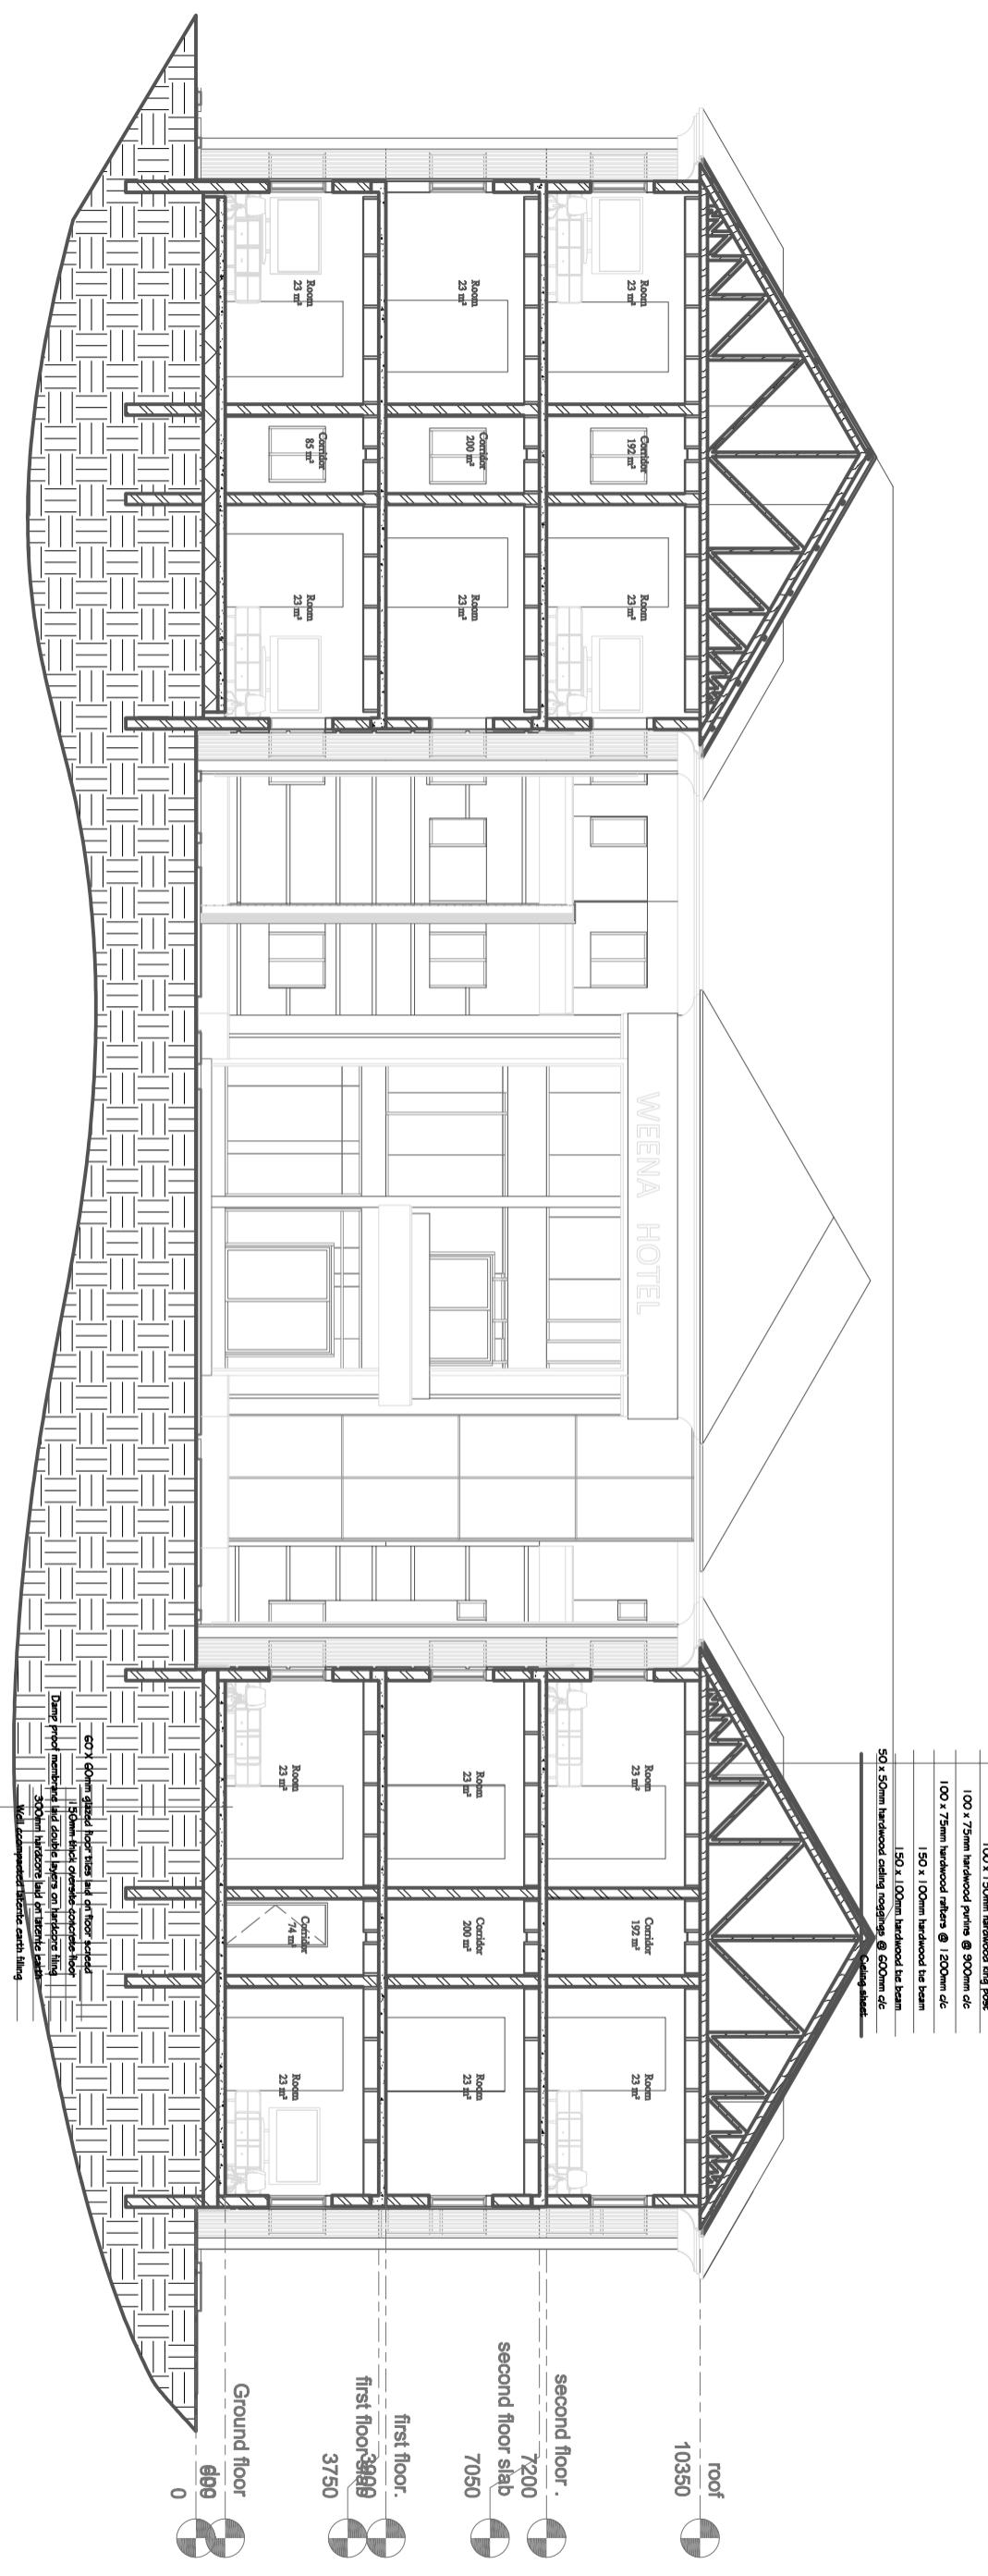

SECTION B-B

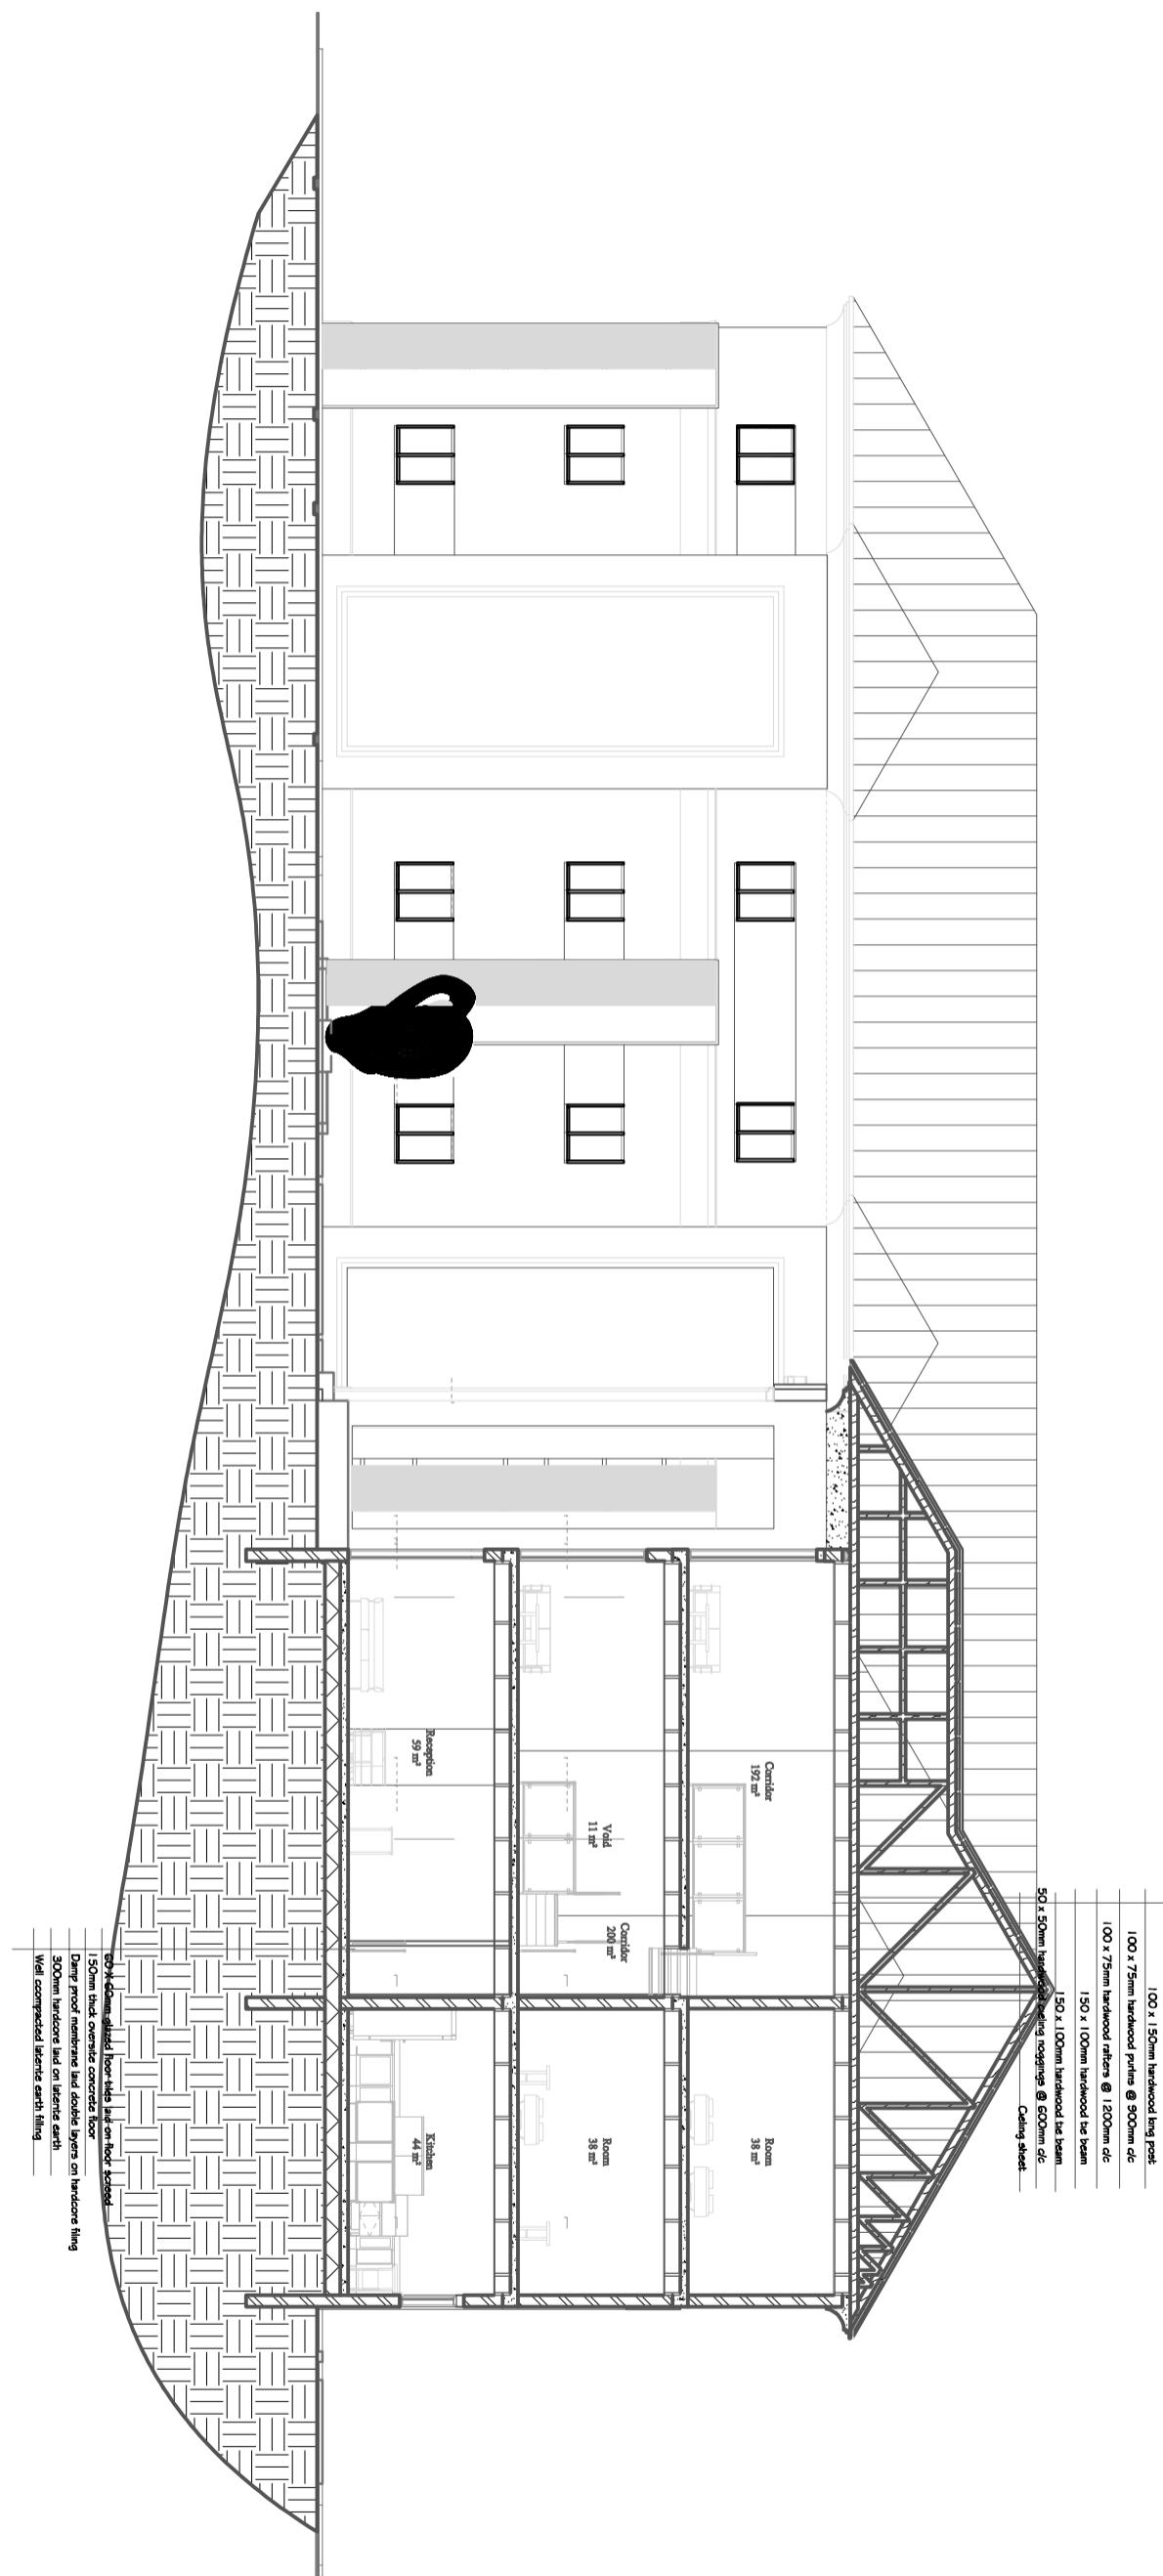

SYMBOL	D1	D2	D3	D4
PROFILE	2100 2230	900 800	1800	
	2100	2100	2100	2100

QTY.	W1	W2	W3	W4	W5
3	118	110	1		

DESCRIPTION

2230x2100mm high double leaf sliding door complete with working detail.